

# PASSARELA - Subtrecho 1.4

| INFORMAÇÕES | | | |
|---|---|---|---|
| FASE | DESCRIÇÃO | VOLUME (m³) | FÔRMA (m²) |
| 1 | BLOCO DE CONCRETO | 4,75 | 10,80 |
| 2 | TRANSVERSINA | 0,35 | 3,25 |
| 3 | BASE PASSARELA | 11,55 | 62,71 |
| 4 | PAREDES | 14,28 | 105,94 |
| TOTAL | | 30,93 | 182,70 |


| RESUMO DE AÇO | | | |
|---|---|---|---|
| AÇO | BIT mm | COMPR m | PESO Kg |
| 60 | 5 | 62 | 10 |
| 50 | 8 | 1229 | 491 |
| 50 | 10 | 4624 | 2913 |
| 50 | 12.5 | 619 | 619 |
| 50 | 16 | 219 | 350 |
| 50 | 25 | 281 | 1123 |
| PESO TOTAL (50) = | | | 5496 |
| PESO TOTAL (60) = | | | 10 |

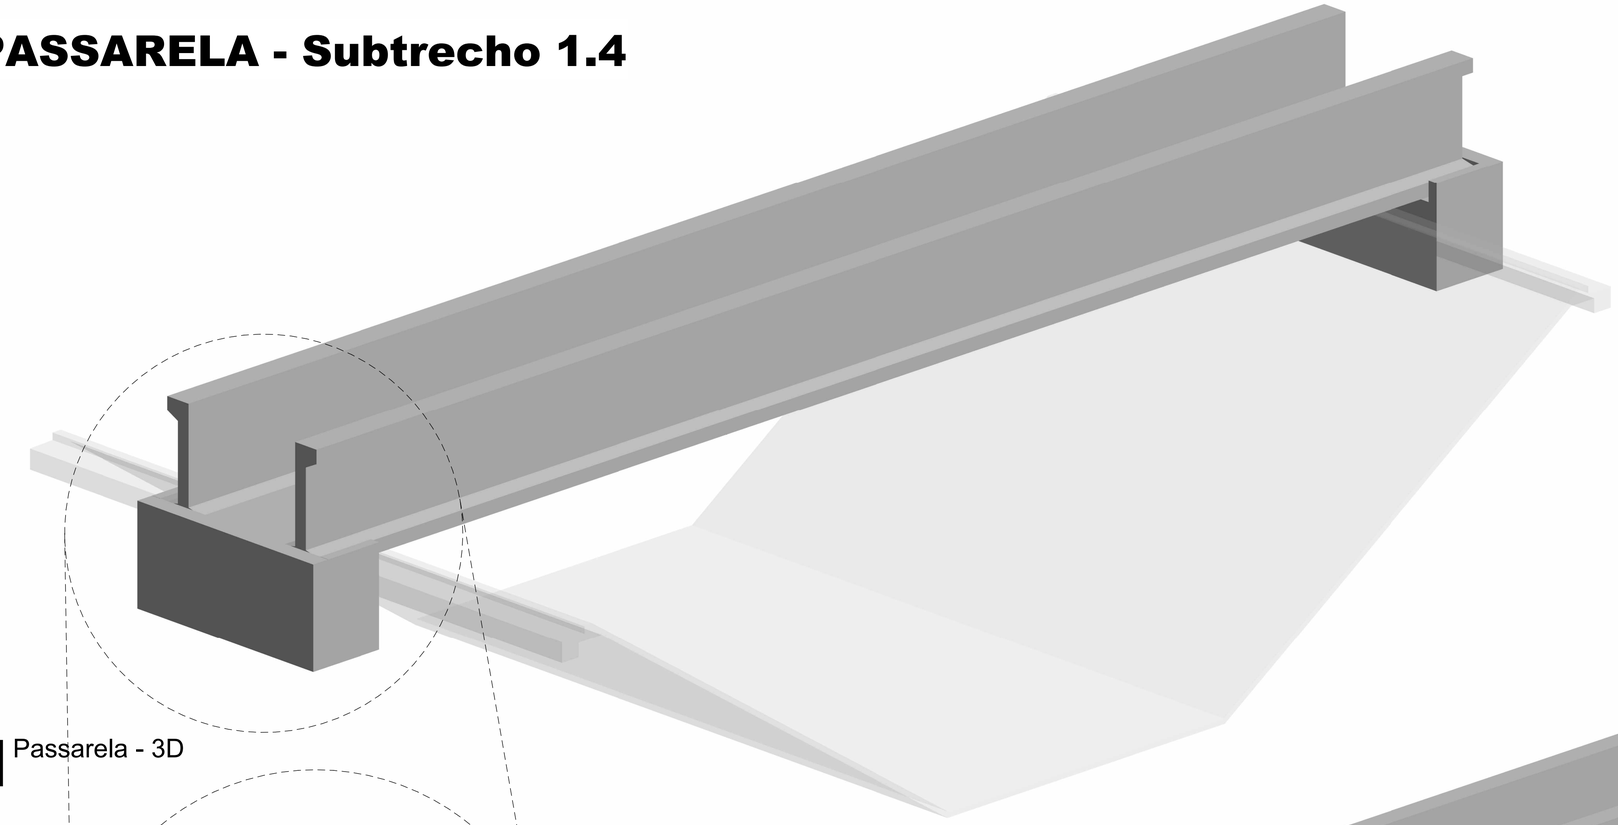

1 Passarela - 3D

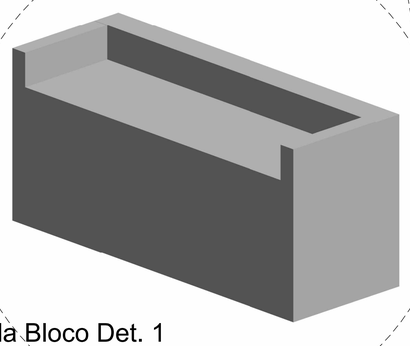


2 Passarela Bloco Det. 1

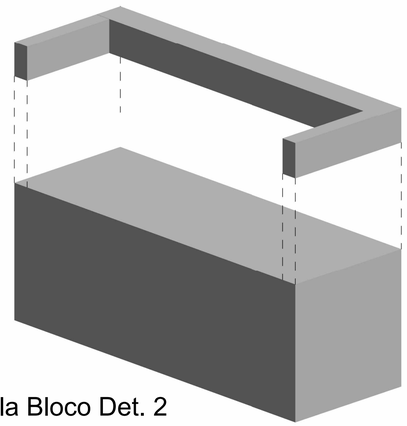

**2- TRANSVERSINA:**
**VOLUME: 0,35m³**

**1- BLOCO DE CONCRETO:**
**VOLUME: 4,75m³**

3 Passarela Bloco Det. 2

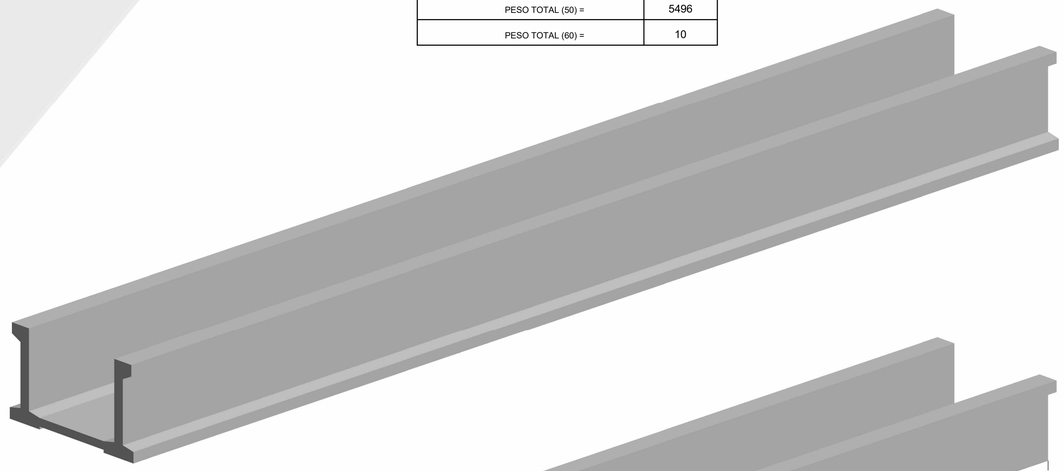

4 Passarela Det. 1

**4- PAREDES:**
**VOLUME: 14,28 m³**

**3- BASE PASSARELA:**
**VOLUME: 11,55 m³**



5 Passarela Det. 2

| CONTROLE DE EXECUÇÃO | | | | | |
|---|---|---|---|---|---|
| OBRA | ESTACA | FUNDAÇÃO | | PONTILHÃO | |
| | | BLOCO | TRANSVERSINA | BASE PASSARELA | PAREDES |
| PASSARELA 20A | 117+700 | | | | |
| PASSARELA 21 | 121+520 | | | | |
| PASSARELA 22A | 130+800 | | | | |
| PASSARELA 22 | 127+480 | | | | |
| PASSARELA 23 | 139+760 | | | | |
| PASSARELA 25 | 144+800 | | | | |

ELABORADO POR CARLOS RAMALHO